


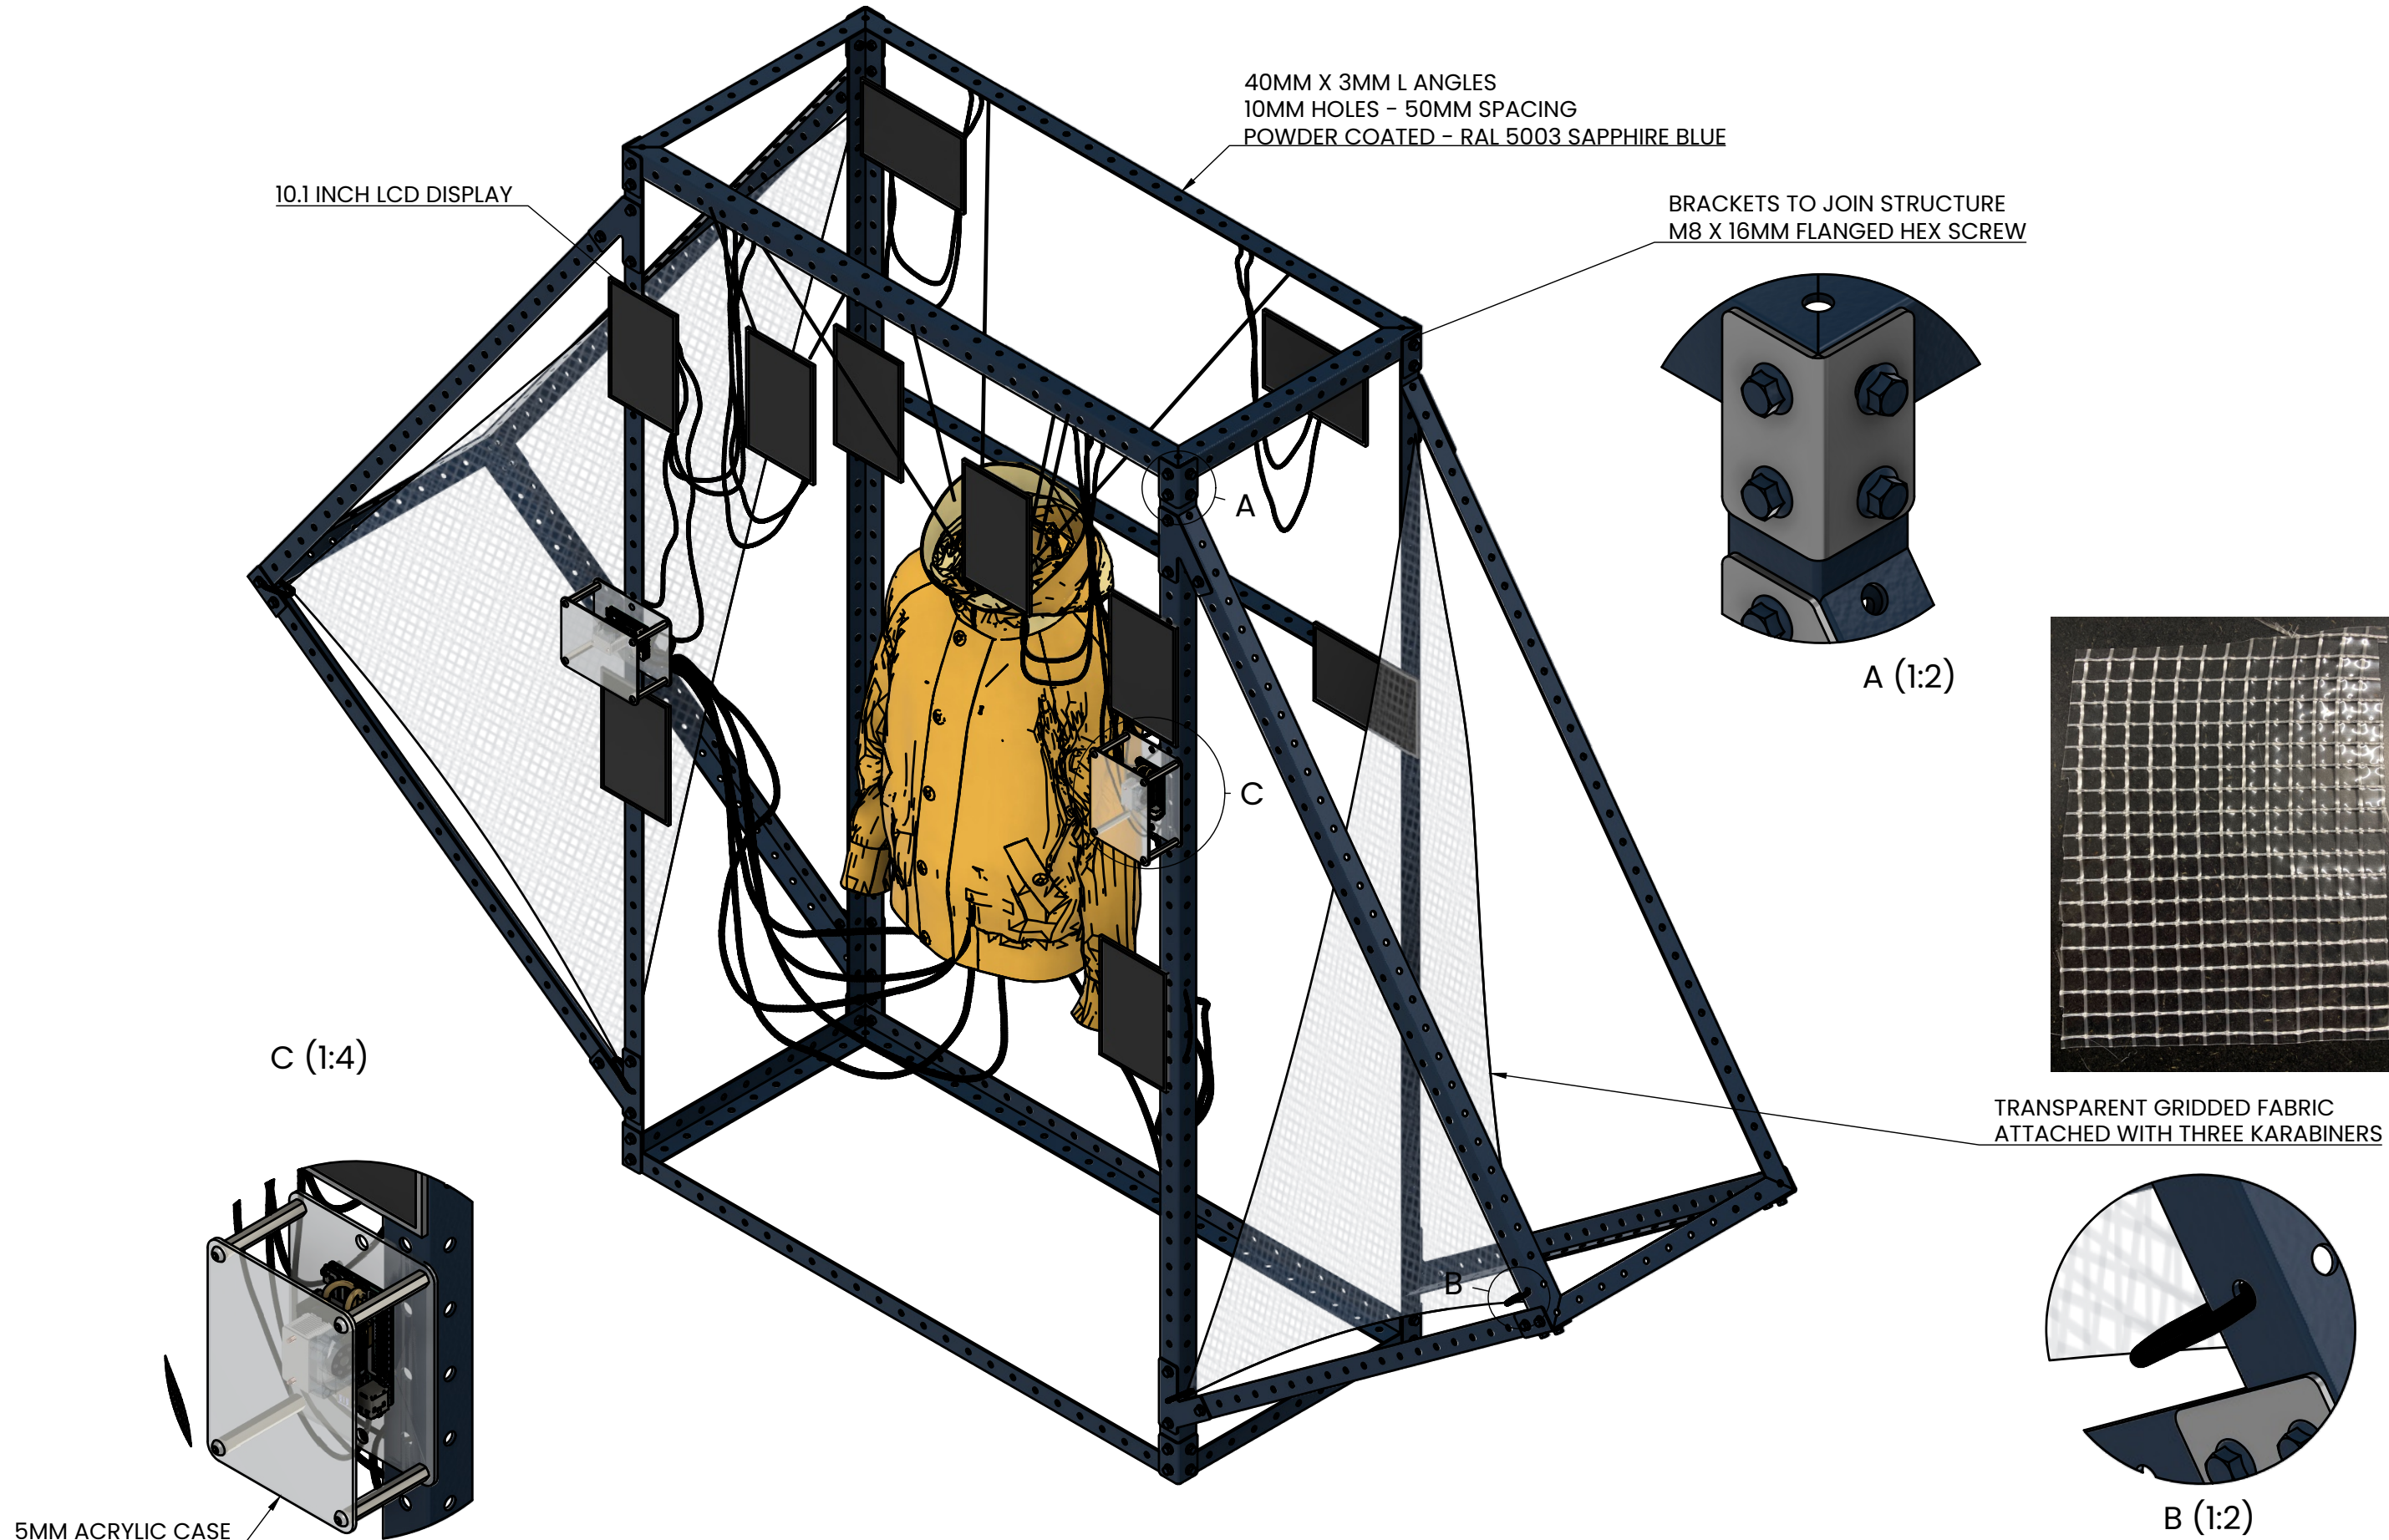

5MM ACRYLIC CASE

10.1 INCH LCD DISPLAY

40MM X 3MM L ANGLES
10MM HOLES - 50MM SPACING
POWDER COATED - RAL 5003 SAPPHIRE BLUE

BRACKETS TO JOIN STRUCTURE
M8 X 16MM FLANGED HEX SCREW


A (1:2)

C (1:4)

B (1:2)

TRANSPARENT GRIDDED FABRIC
ATTACHED WITH THREE KARABINERS

TITLE WINDOW 10	VERSION # V_01	THIS DRAWING IS INTENDED FOR THE NAMED ONLY. IT CONTAINS INFORMATION WHICH MAY BE CONFIDENTIAL & WHICH MAY ALSO BE PRIVILEGED, UNLESS YOU ARE THE NAMED ADDRESSEE (OR AUTHORISED TO RECEIVE IT FOR THE ADDRESSEE) YOU MAY NOT COPY OR USE IT, OR DISCLOSE IT TO ANYONE ELSE.
PROJECT STONE ISLAND MARINA SELFRIDGES	DATE 28_03_2025	
CLIENT CHARLIE PARKER PRODUCTIONS	DRAWN BY LEWIS STEPHENS	

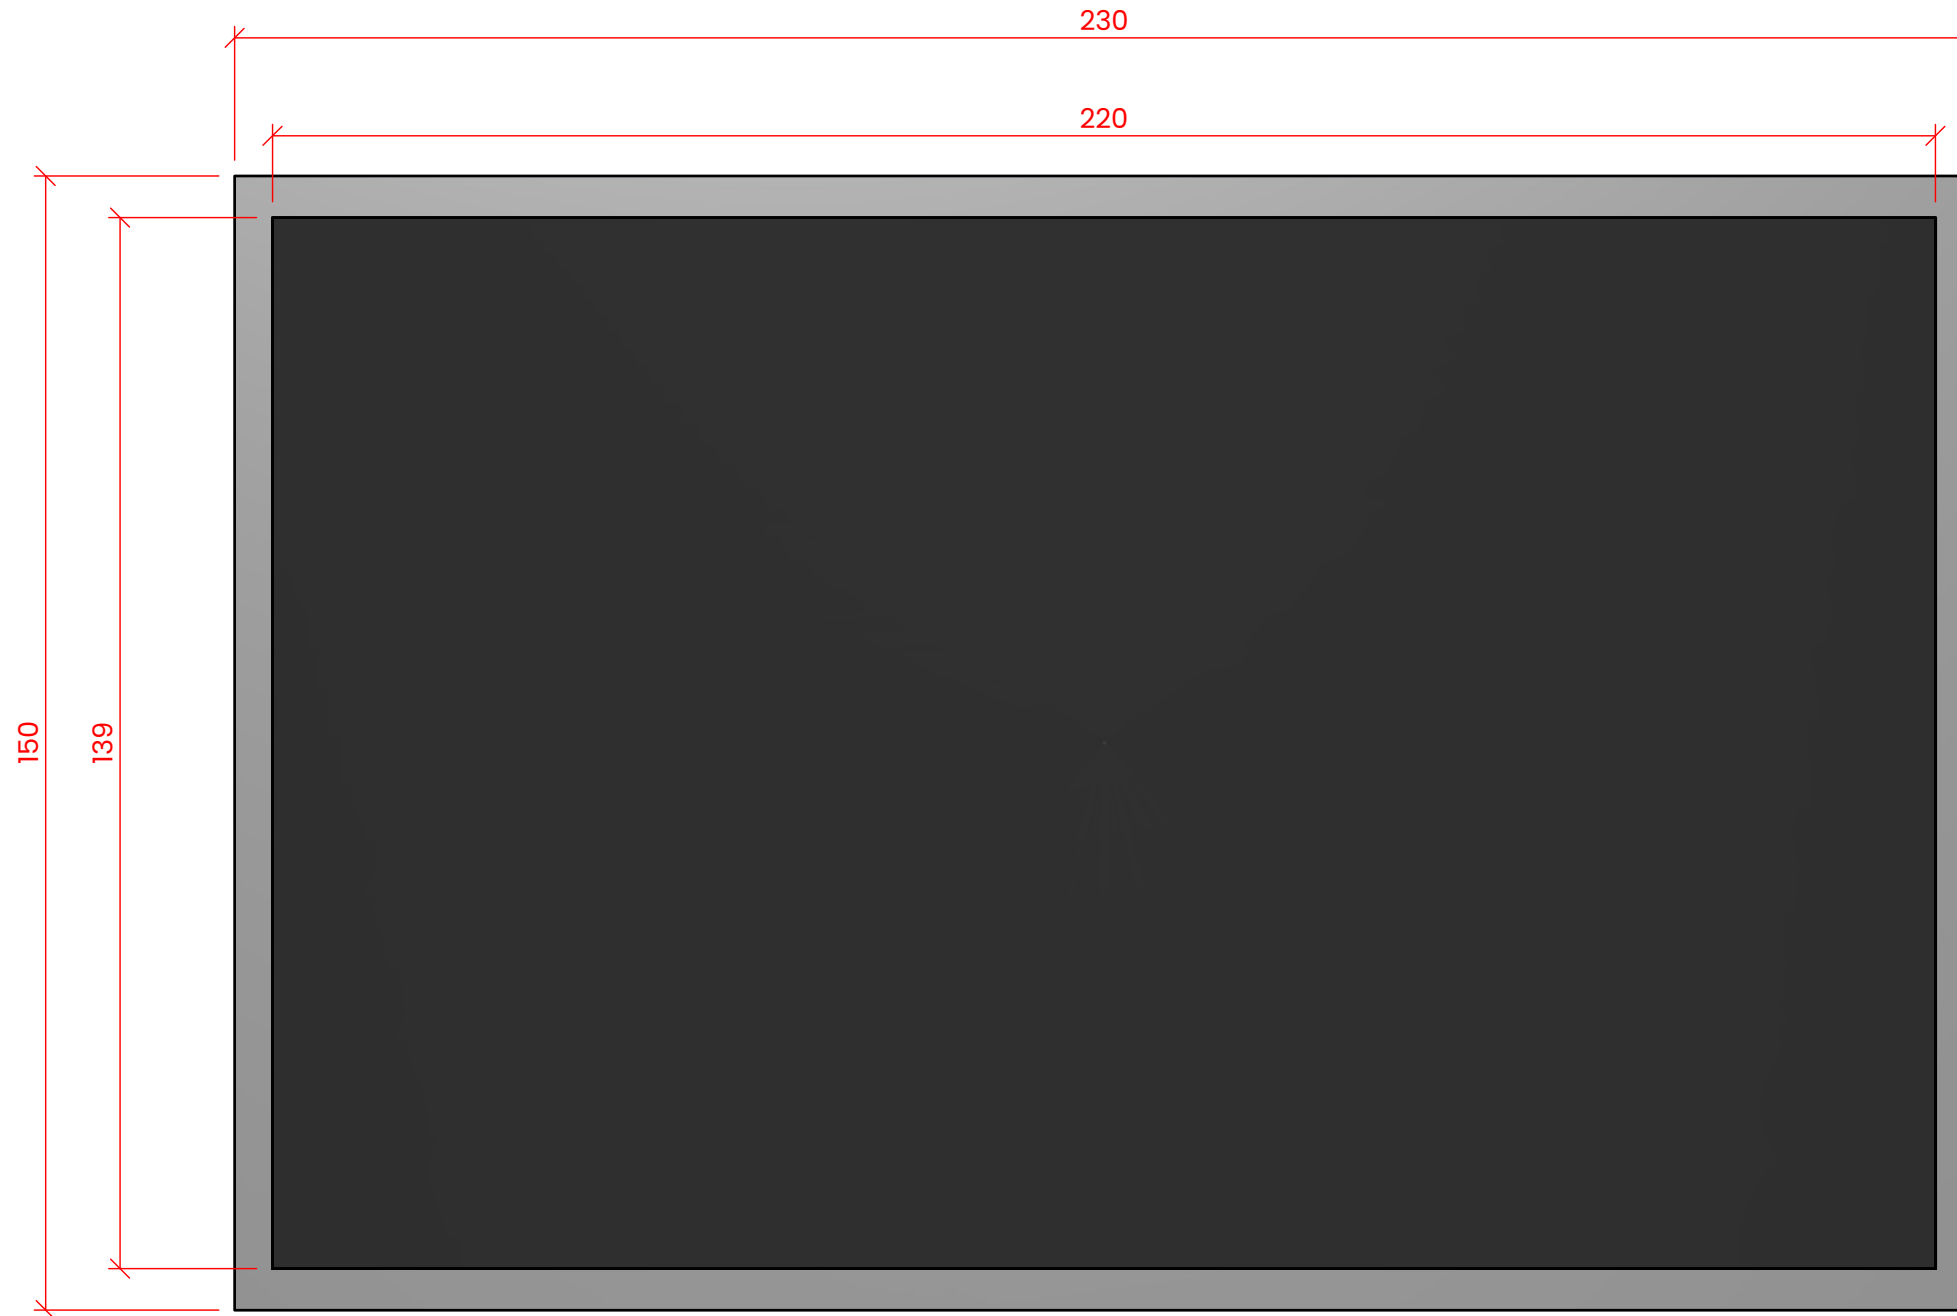


10.1" TFT-LCD Screen
Display Ratio - 10:16
Resolution - 800 x 1280
Colour Depth - 24-bit
Power Draw - 11.5W

TITLE WINDOW 10	VERSION # V_01	THIS DRAWING IS INTENDED FOR THE NAMED ONLY. IT CONTAINS INFORMATION WHICH MAY BE CONFIDENTIAL & WHICH MAY ALSO BE PRIVILEGED. UNLESS YOU ARE THE NAMED ADDRESSEE (OR AUTHORISED TO RECEIVE IT FOR THE ADDRESSEE) YOU MAY NOT COPY OR USE IT, OR DISCLOSE IT TO ANYONE ELSE.
PROJECT STONE ISLAND MARINA SELFRIDGES	DATE 28_03_2025	
CLIENT CHARLIE PARKER PRODUCTIONS	DRAWN BY LEWIS STEPHENS	



RENDER SURFACE FINISH



RAL 085 85 20
HELBLOND

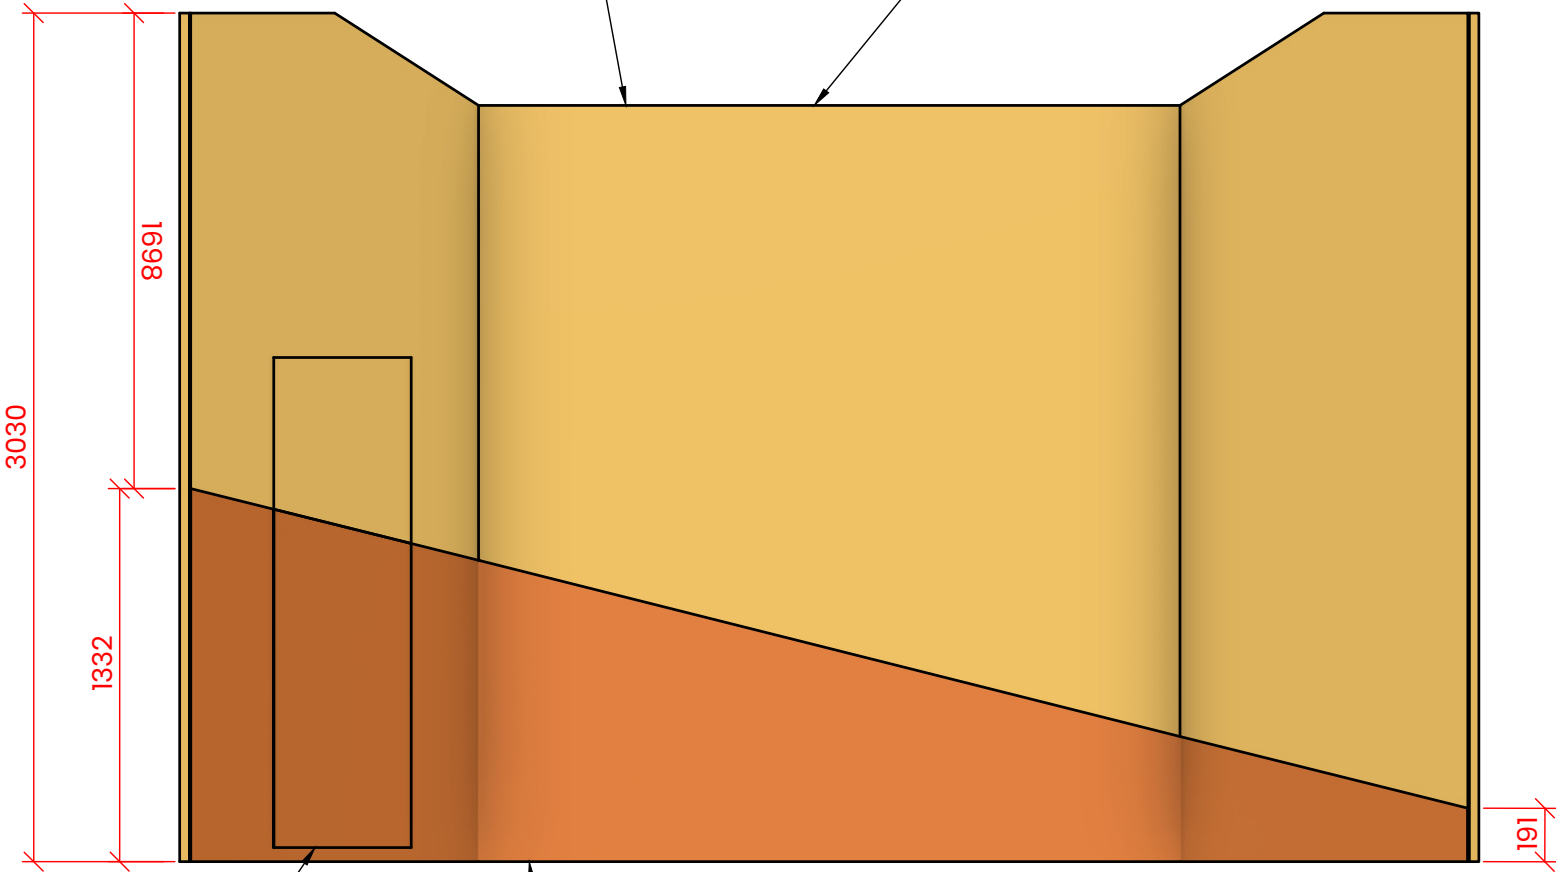

RAL 2000
GELBORANGE

MADE FROM LIGHTWEIGHT PLYWOOD WITH 18MM PLYWOOD FRAMEWORK

ALL PLYWOOD TO BE FR CLEAR COATED

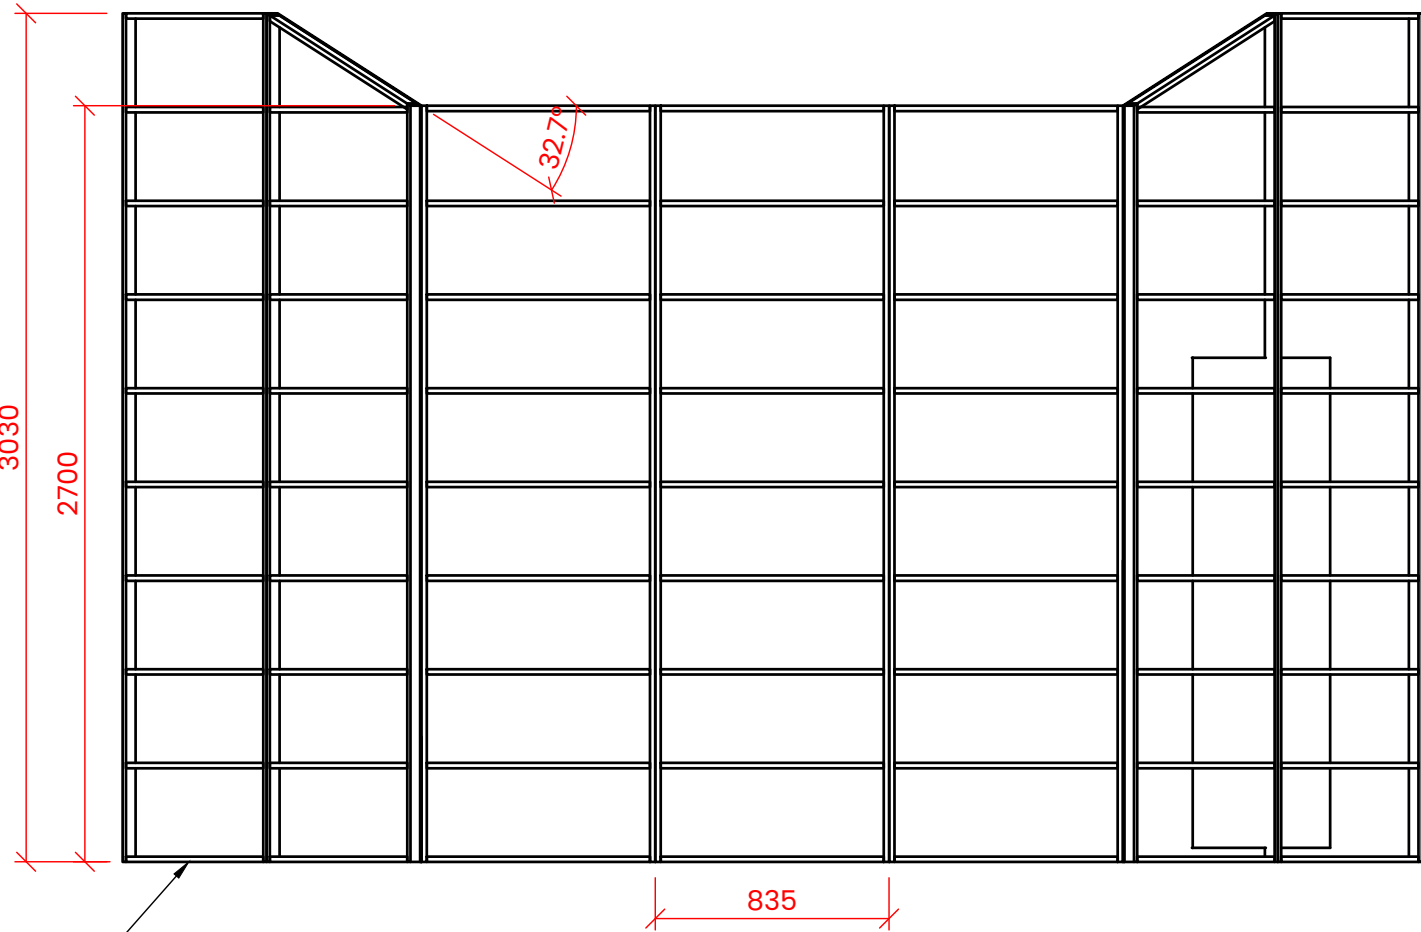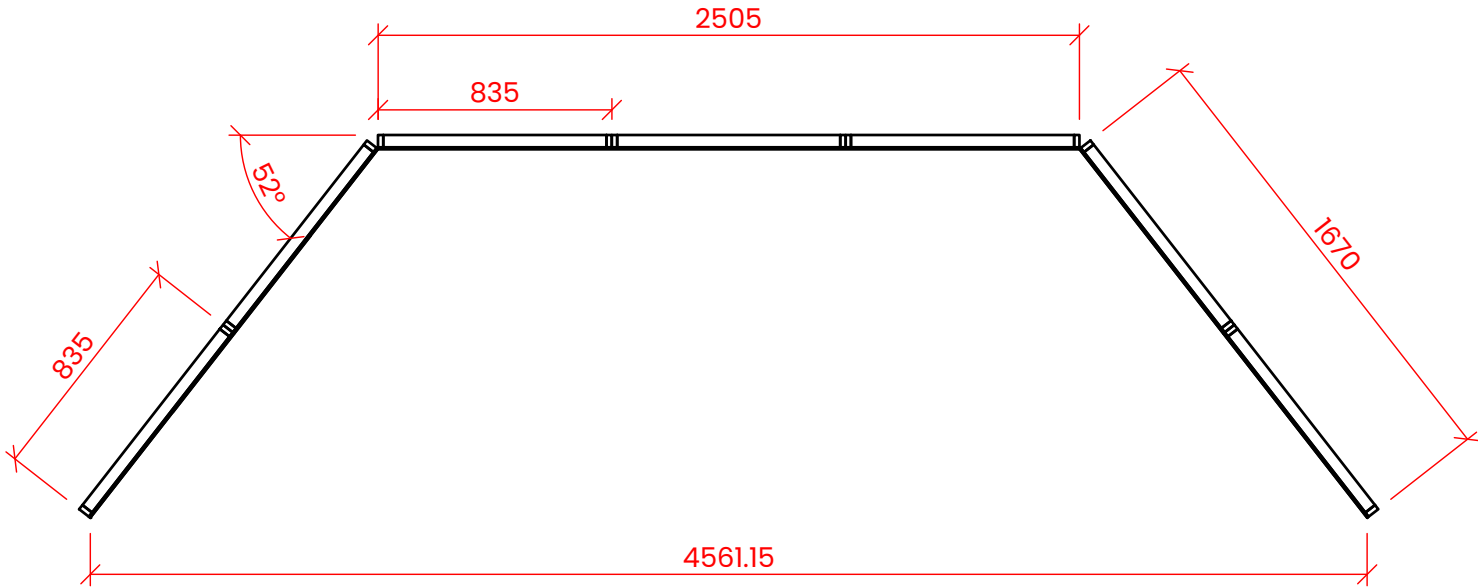


TITLE WINDOW 10	VERSION # V_01	THIS DRAWING IS INTENDED FOR THE NAMED ONLY. IT CONTAINS INFORMATION WHICH MAY BE CONFIDENTIAL & WHICH MAY ALSO BE PRIVILEGED, UNLESS YOU ARE THE NAMED ADDRESSEE (OR AUTHORISED TO RECEIVE IT FOR THE ADDRESSEE) YOU MAY NOT COPY OR USE IT, OR DISCLOSE IT TO ANYONE ELSE.
PROJECT STONE ISLAND MARINA SELFRIDGES	DATE 28_03_2025	
CLIENT CHARLIE PARKER PRODUCTIONS	DRAWN BY LEWIS STEPHENS	

STONE ISLAND
MARINA

DESIGNER STREET ROOM ON 1

TITLE WINDOW 10	VERSION # V_01	THIS DRAWING IS INTENDED FOR THE NAMED ONLY. IT CONTAINS INFORMATION WHICH MAY BE CONFIDENTIAL & WHICH MAY ALSO BE PRIVILEGED. UNLESS YOU ARE THE NAMED ADDRESSEE (OR AUTHORISED TO RECEIVE IT FOR THE ADDRESSEE) YOU MAY NOT COPY OR USE IT, OR DISCLOSE IT TO ANYONE ELSE.
PROJECT STONE ISLAND MARINA SELFRIDGES	DATE 28_03_2025	
CLIENT CHARLIE PARKER PRODUCTIONS	DRAWN BY LEWIS STEPHENS	

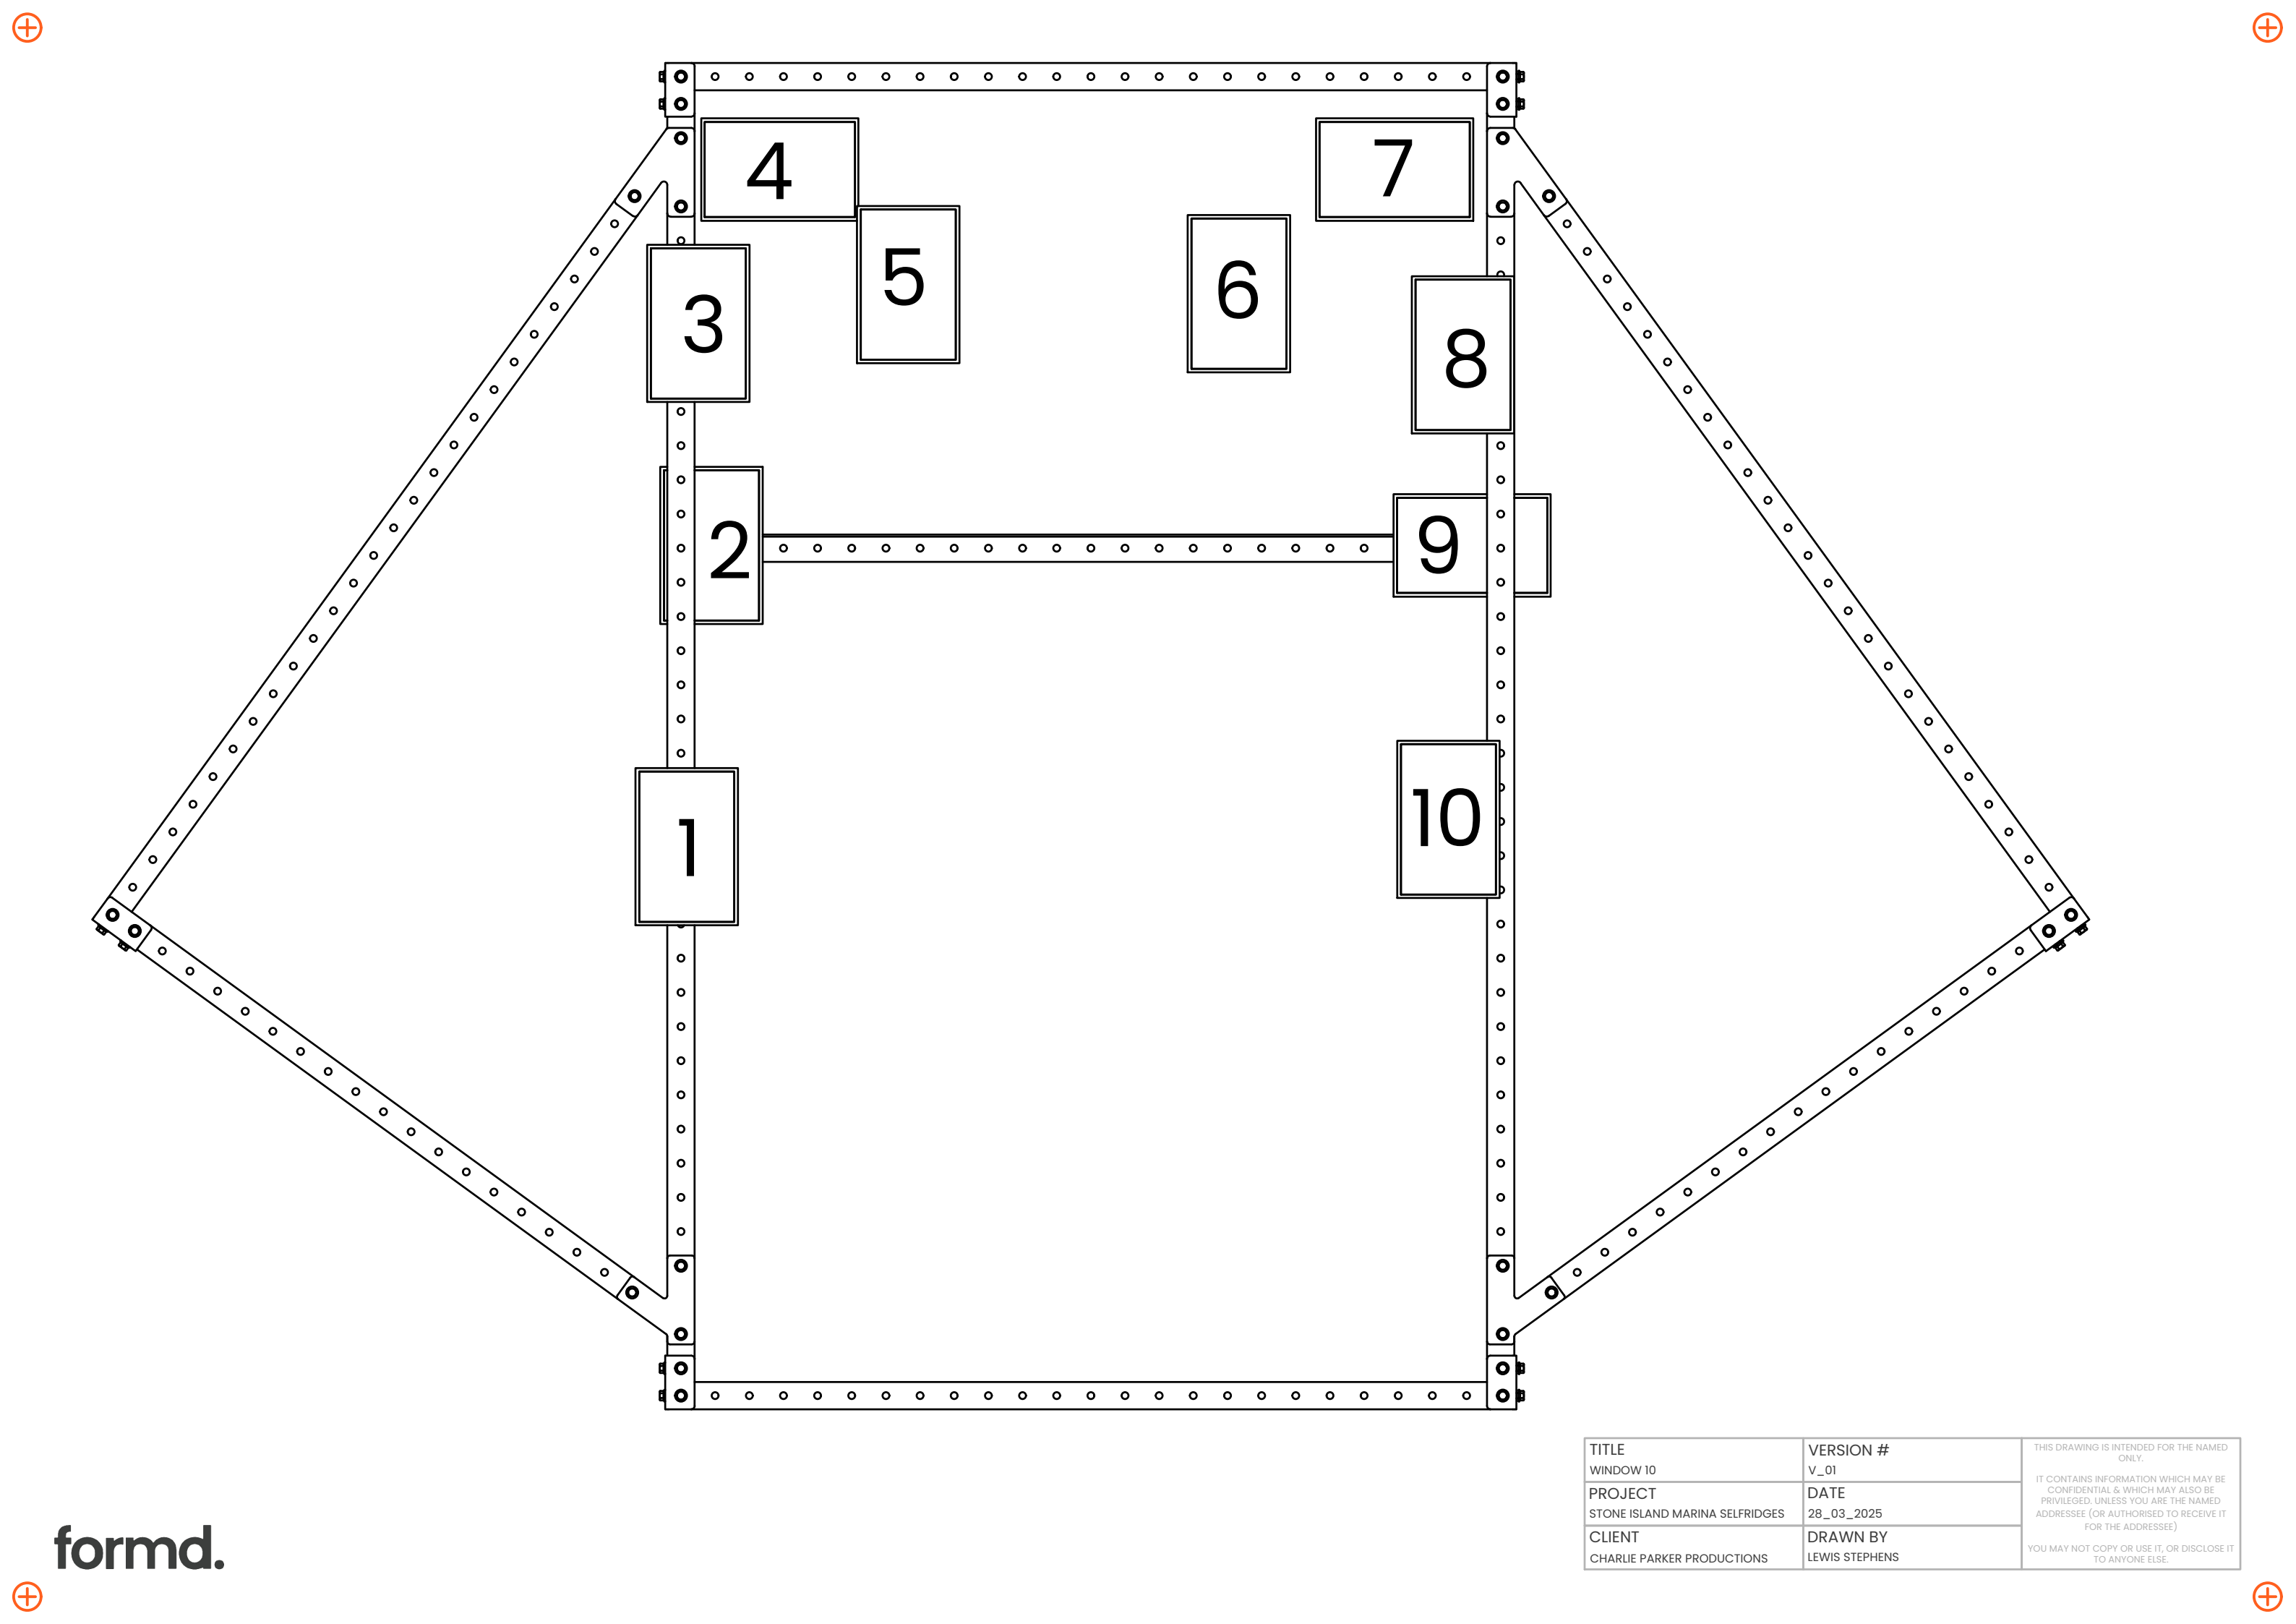

TITLE WINDOW 10	VERSION # V_01	THIS DRAWING IS INTENDED FOR THE NAMED ONLY. IT CONTAINS INFORMATION WHICH MAY BE CONFIDENTIAL & WHICH MAY ALSO BE PRIVILEGED. UNLESS YOU ARE THE NAMED ADDRESSEE (OR AUTHORISED TO RECEIVE IT FOR THE ADDRESSEE) YOU MAY NOT COPY OR USE IT, OR DISCLOSE IT TO ANYONE ELSE.
PROJECT STONE ISLAND MARINA SELFRIDGES	DATE 28_03_2025	
CLIENT CHARLIE PARKER PRODUCTIONS	DRAWN BY LEWIS STEPHENS	